

MODIFICACIONES:		
V. No.	Fecha	Descripción
04	07.03.2025	Actualización de detalles constructivos de vivienda UE1 por ajustes de conexión y calidad
05	28.03.2025	Actualización de la especificación de brazo para puertas de mueble alto de cocina
06	07.07.2025	01. Se actualiza especificación incluyendo tipo de conexión y referencia de espesores interiores en los detalles de cocina. Torre 1 y Torre 2. 02. Se incluyen detalles constructivos de vivienda para Torre 2-U2
07	18.07.2025	01. Se incluye salpicadero en mueble de cocina tipo isla

AMARILLO S.A.
VÁLIDO PARA CONSTRUIR
18.07.2025

COORDINADOR Maia Alejandra Celeste Mora
VERSIÓN 07

CONTENIDO:
DETALLES DE VIVIENDA
 Detalles de Cocinas
 Detalle Cocina CO-01 - Apt A
 01. Corte A
 02. Corte B
 03. Corte C

VERSIÓN: 07 **CONSECUTIVO:** APT- 581B




ARCHIVO REVIT: Autodesk-DocRevit_NOGAL_PRN\19\37\NOG-APT-581B\

APROBÓ:

Maia Alejandra Celeste Mora
COORDINADOR DE DISEÑO

FECHA: 18.07.2025 **DIBUJO:** A.P.Q.
 ESCALA: 1: 25

NOG-ARQ- APT- 581B
CO01-Apt A

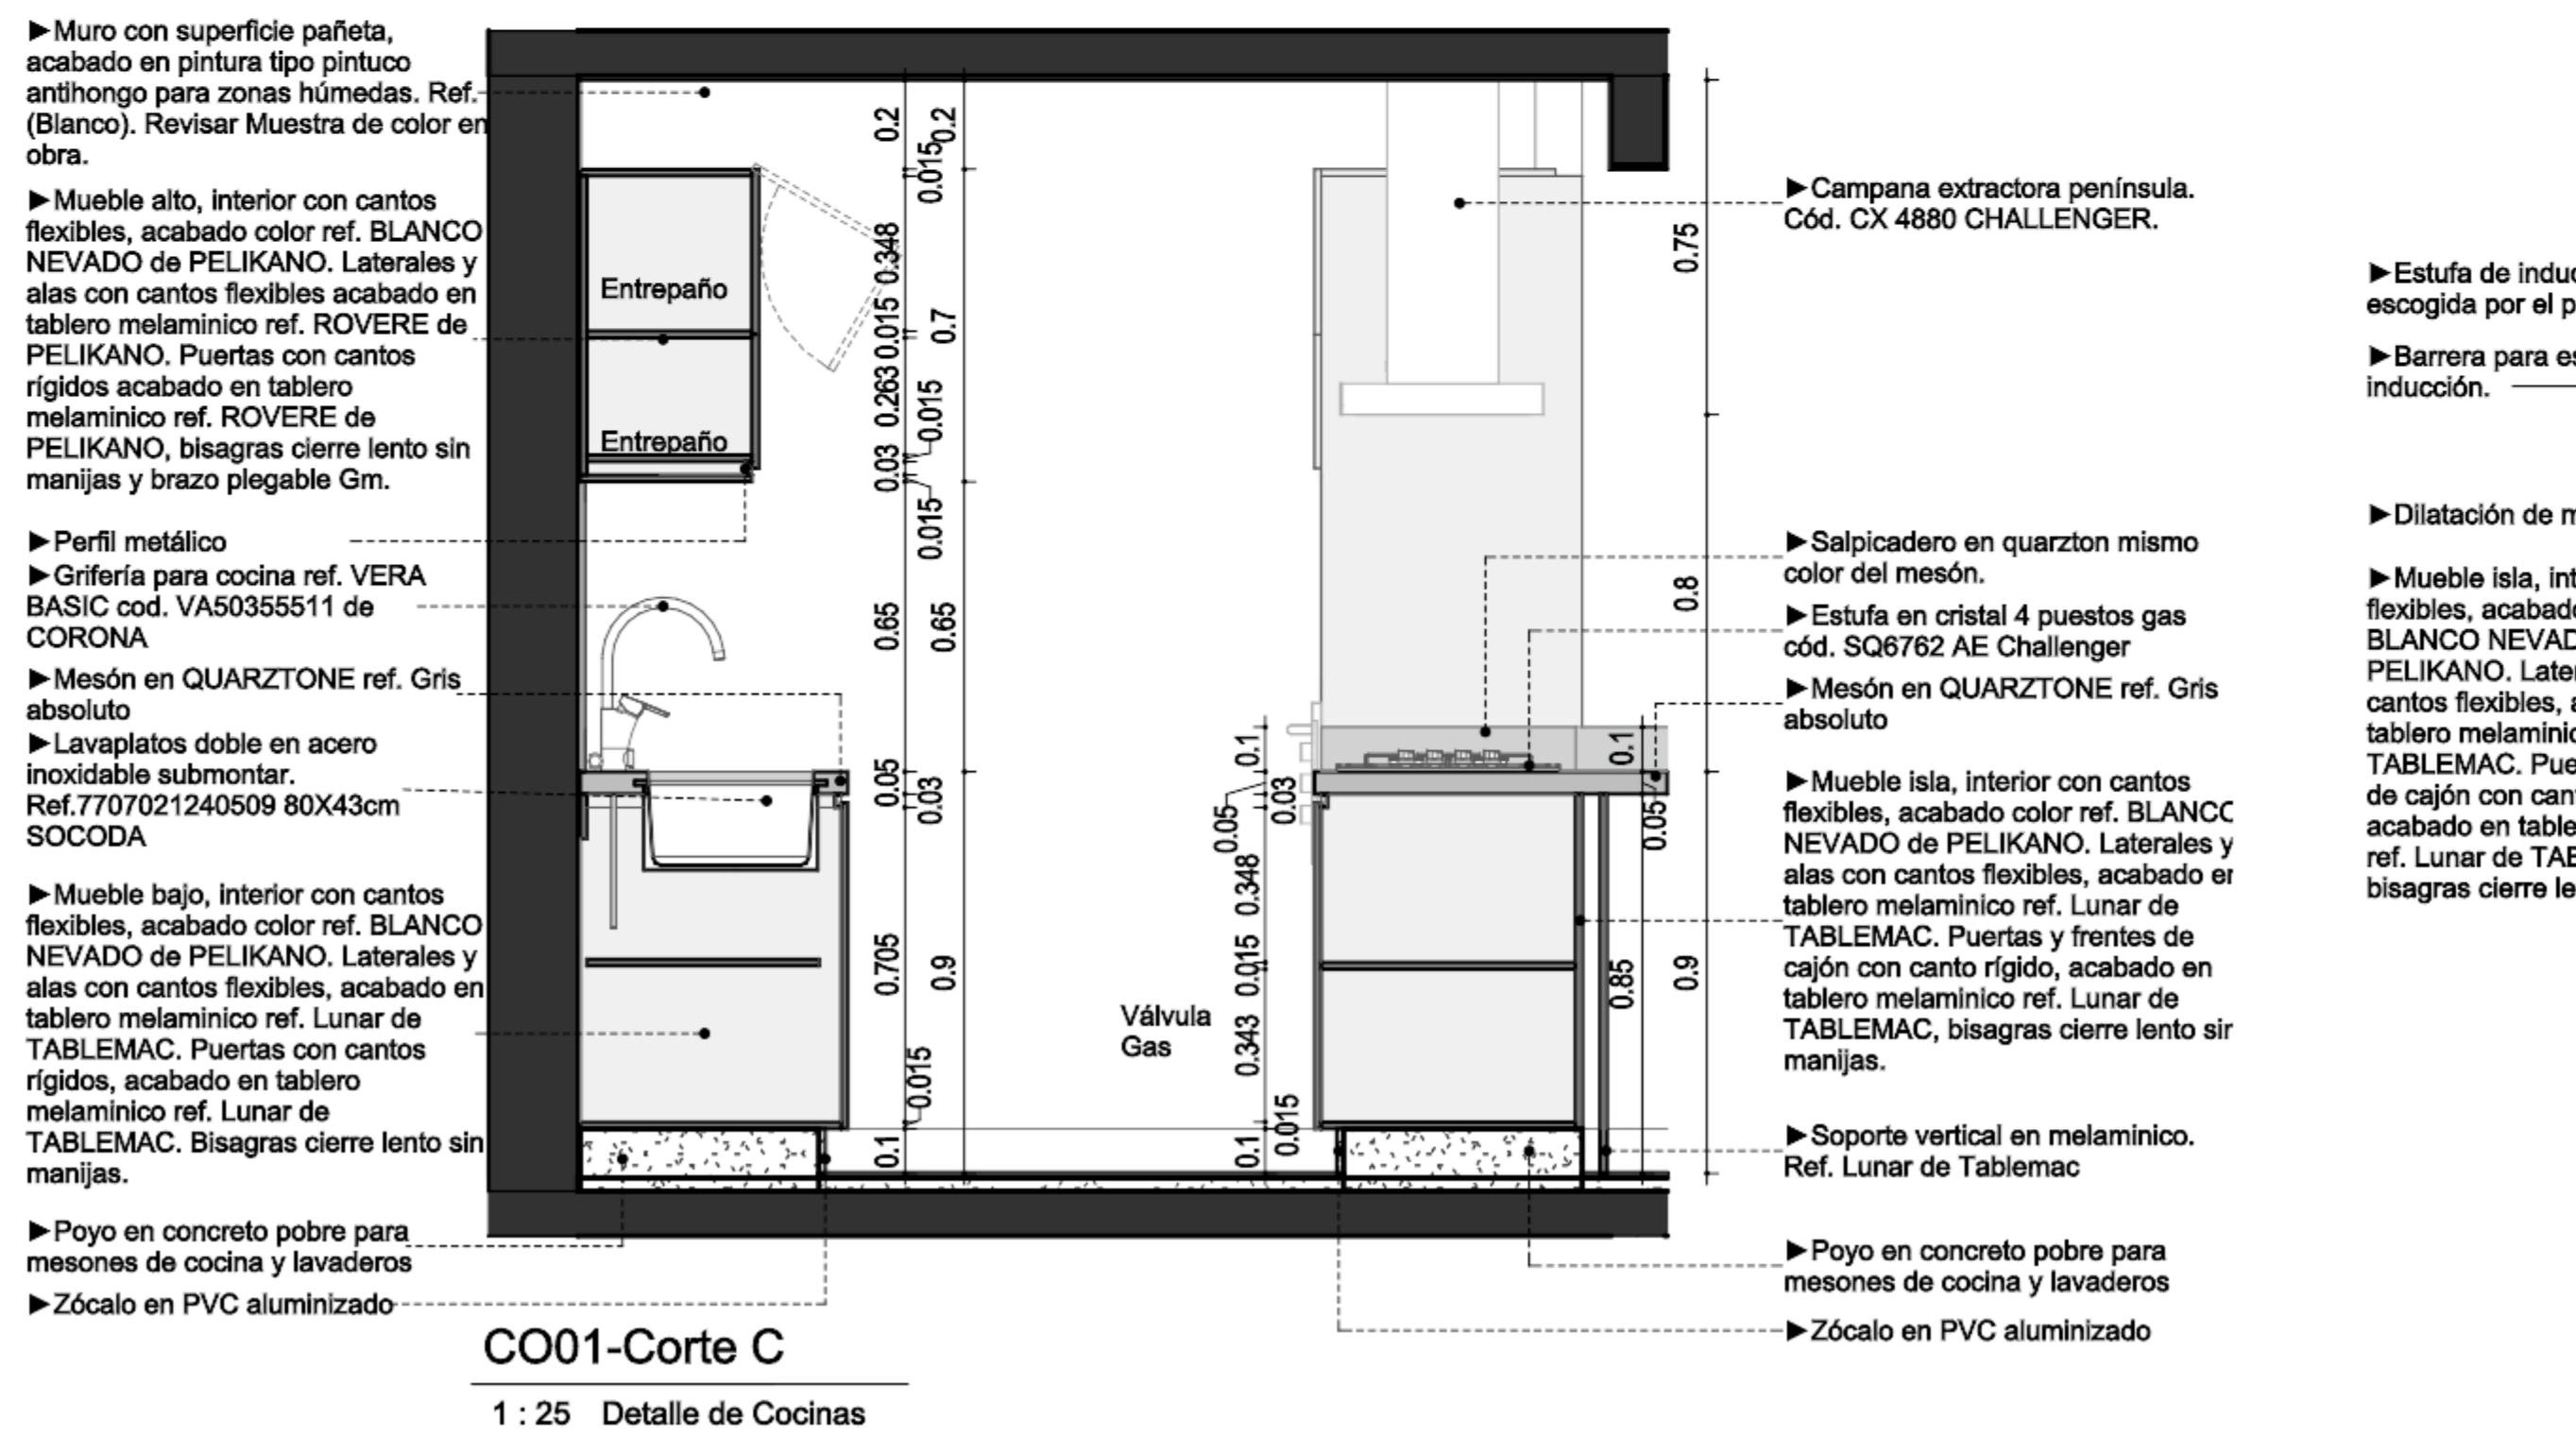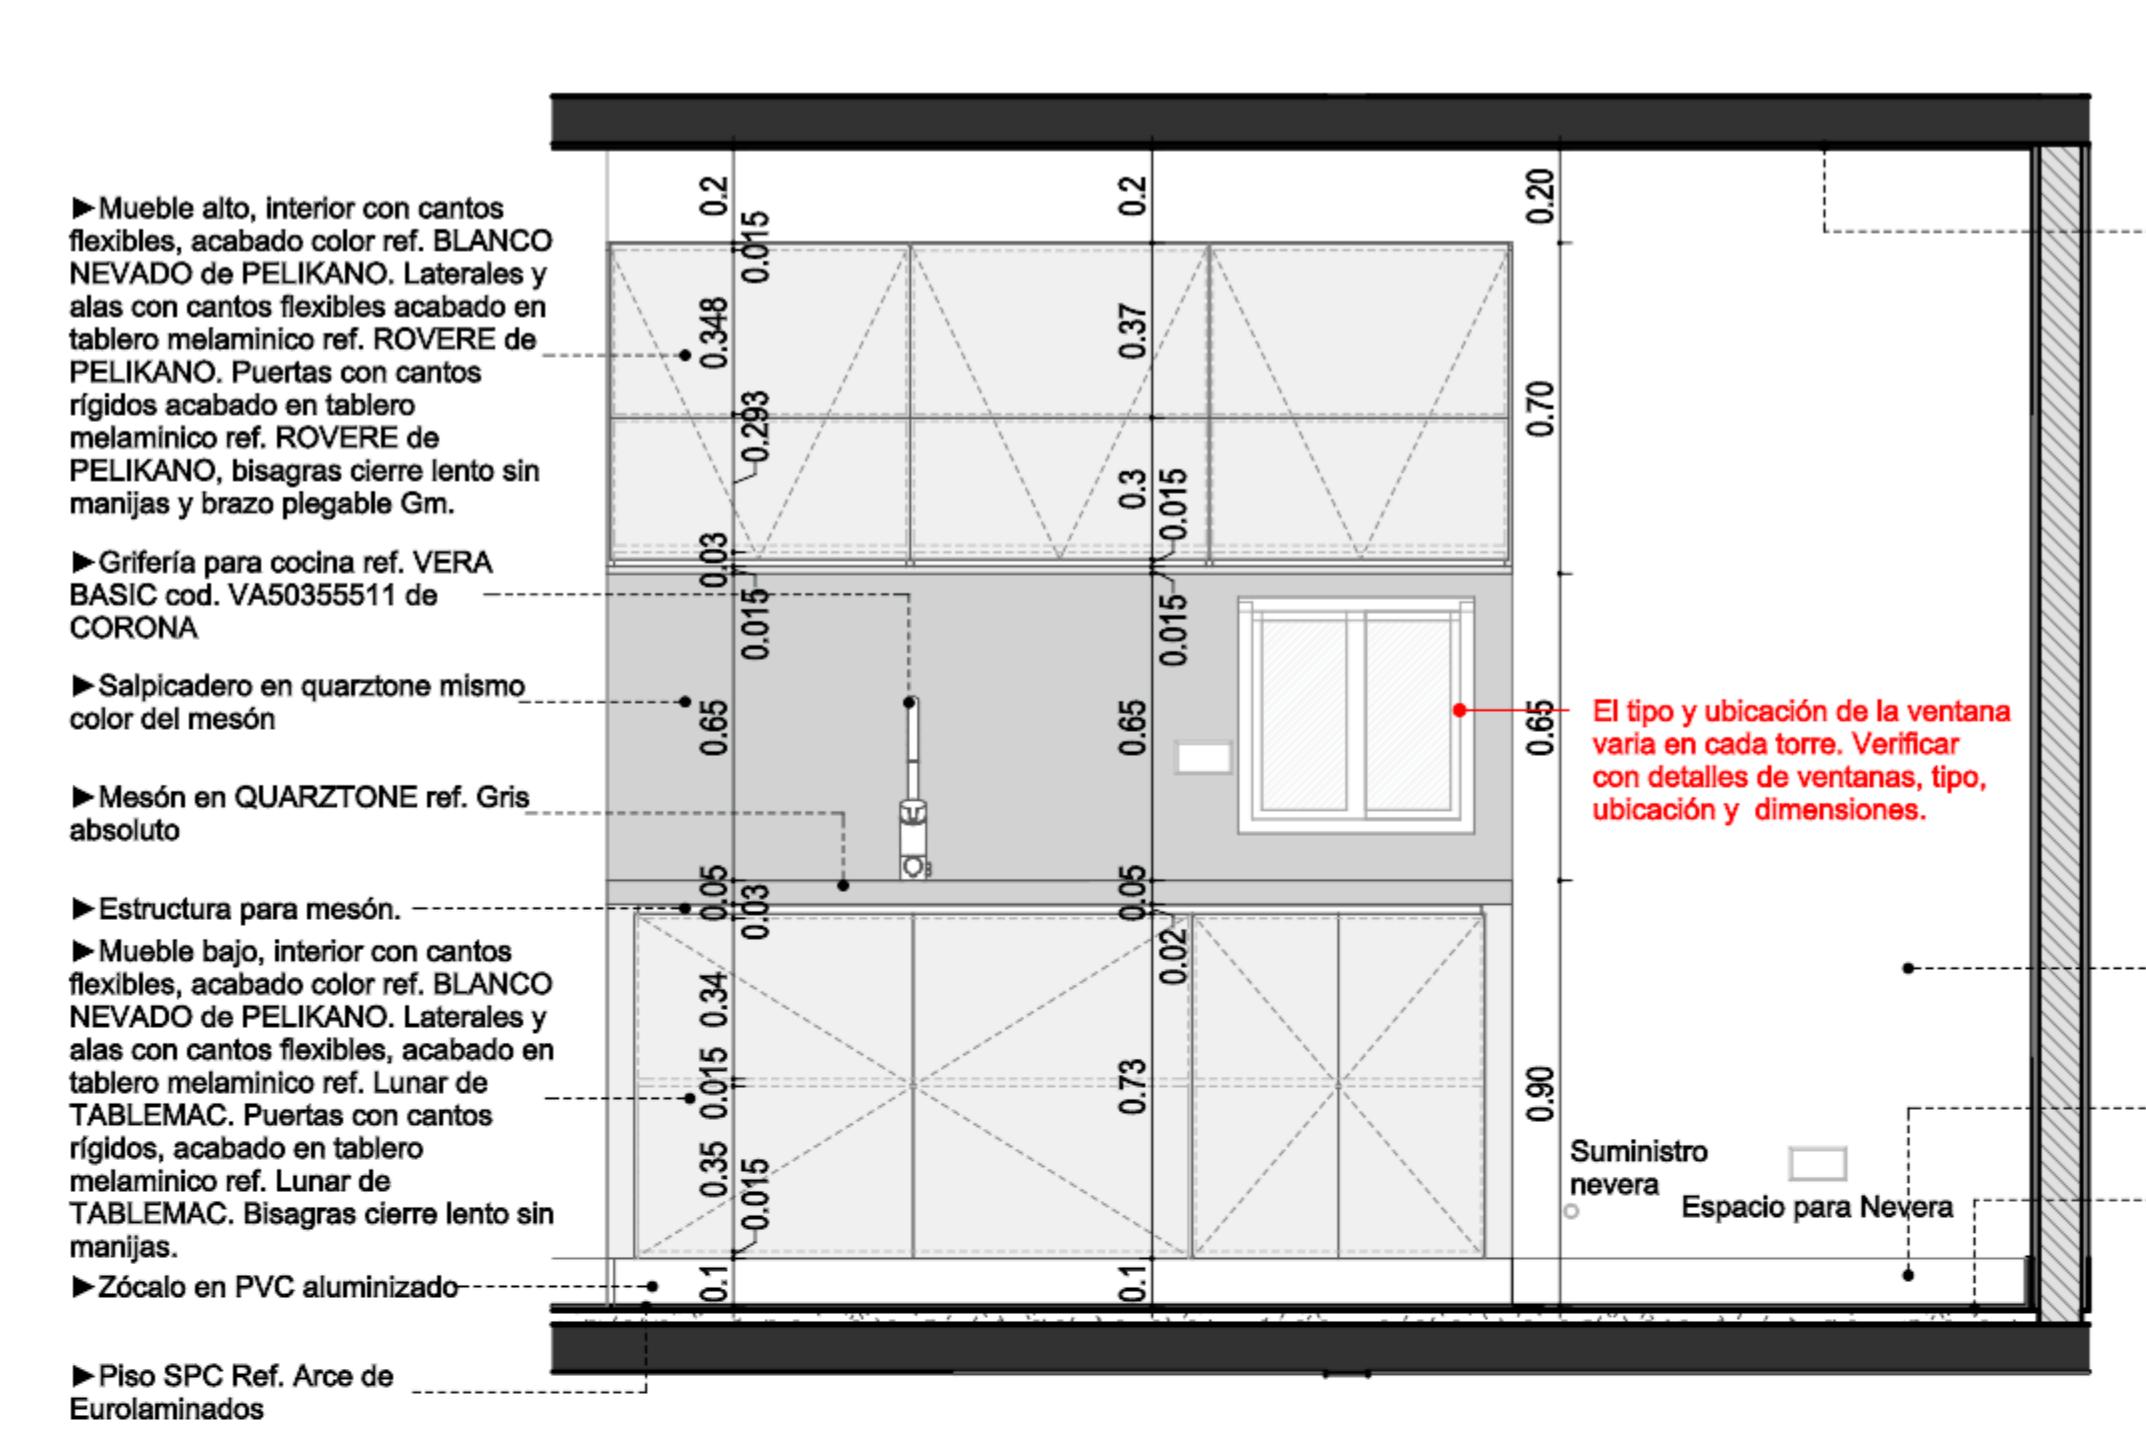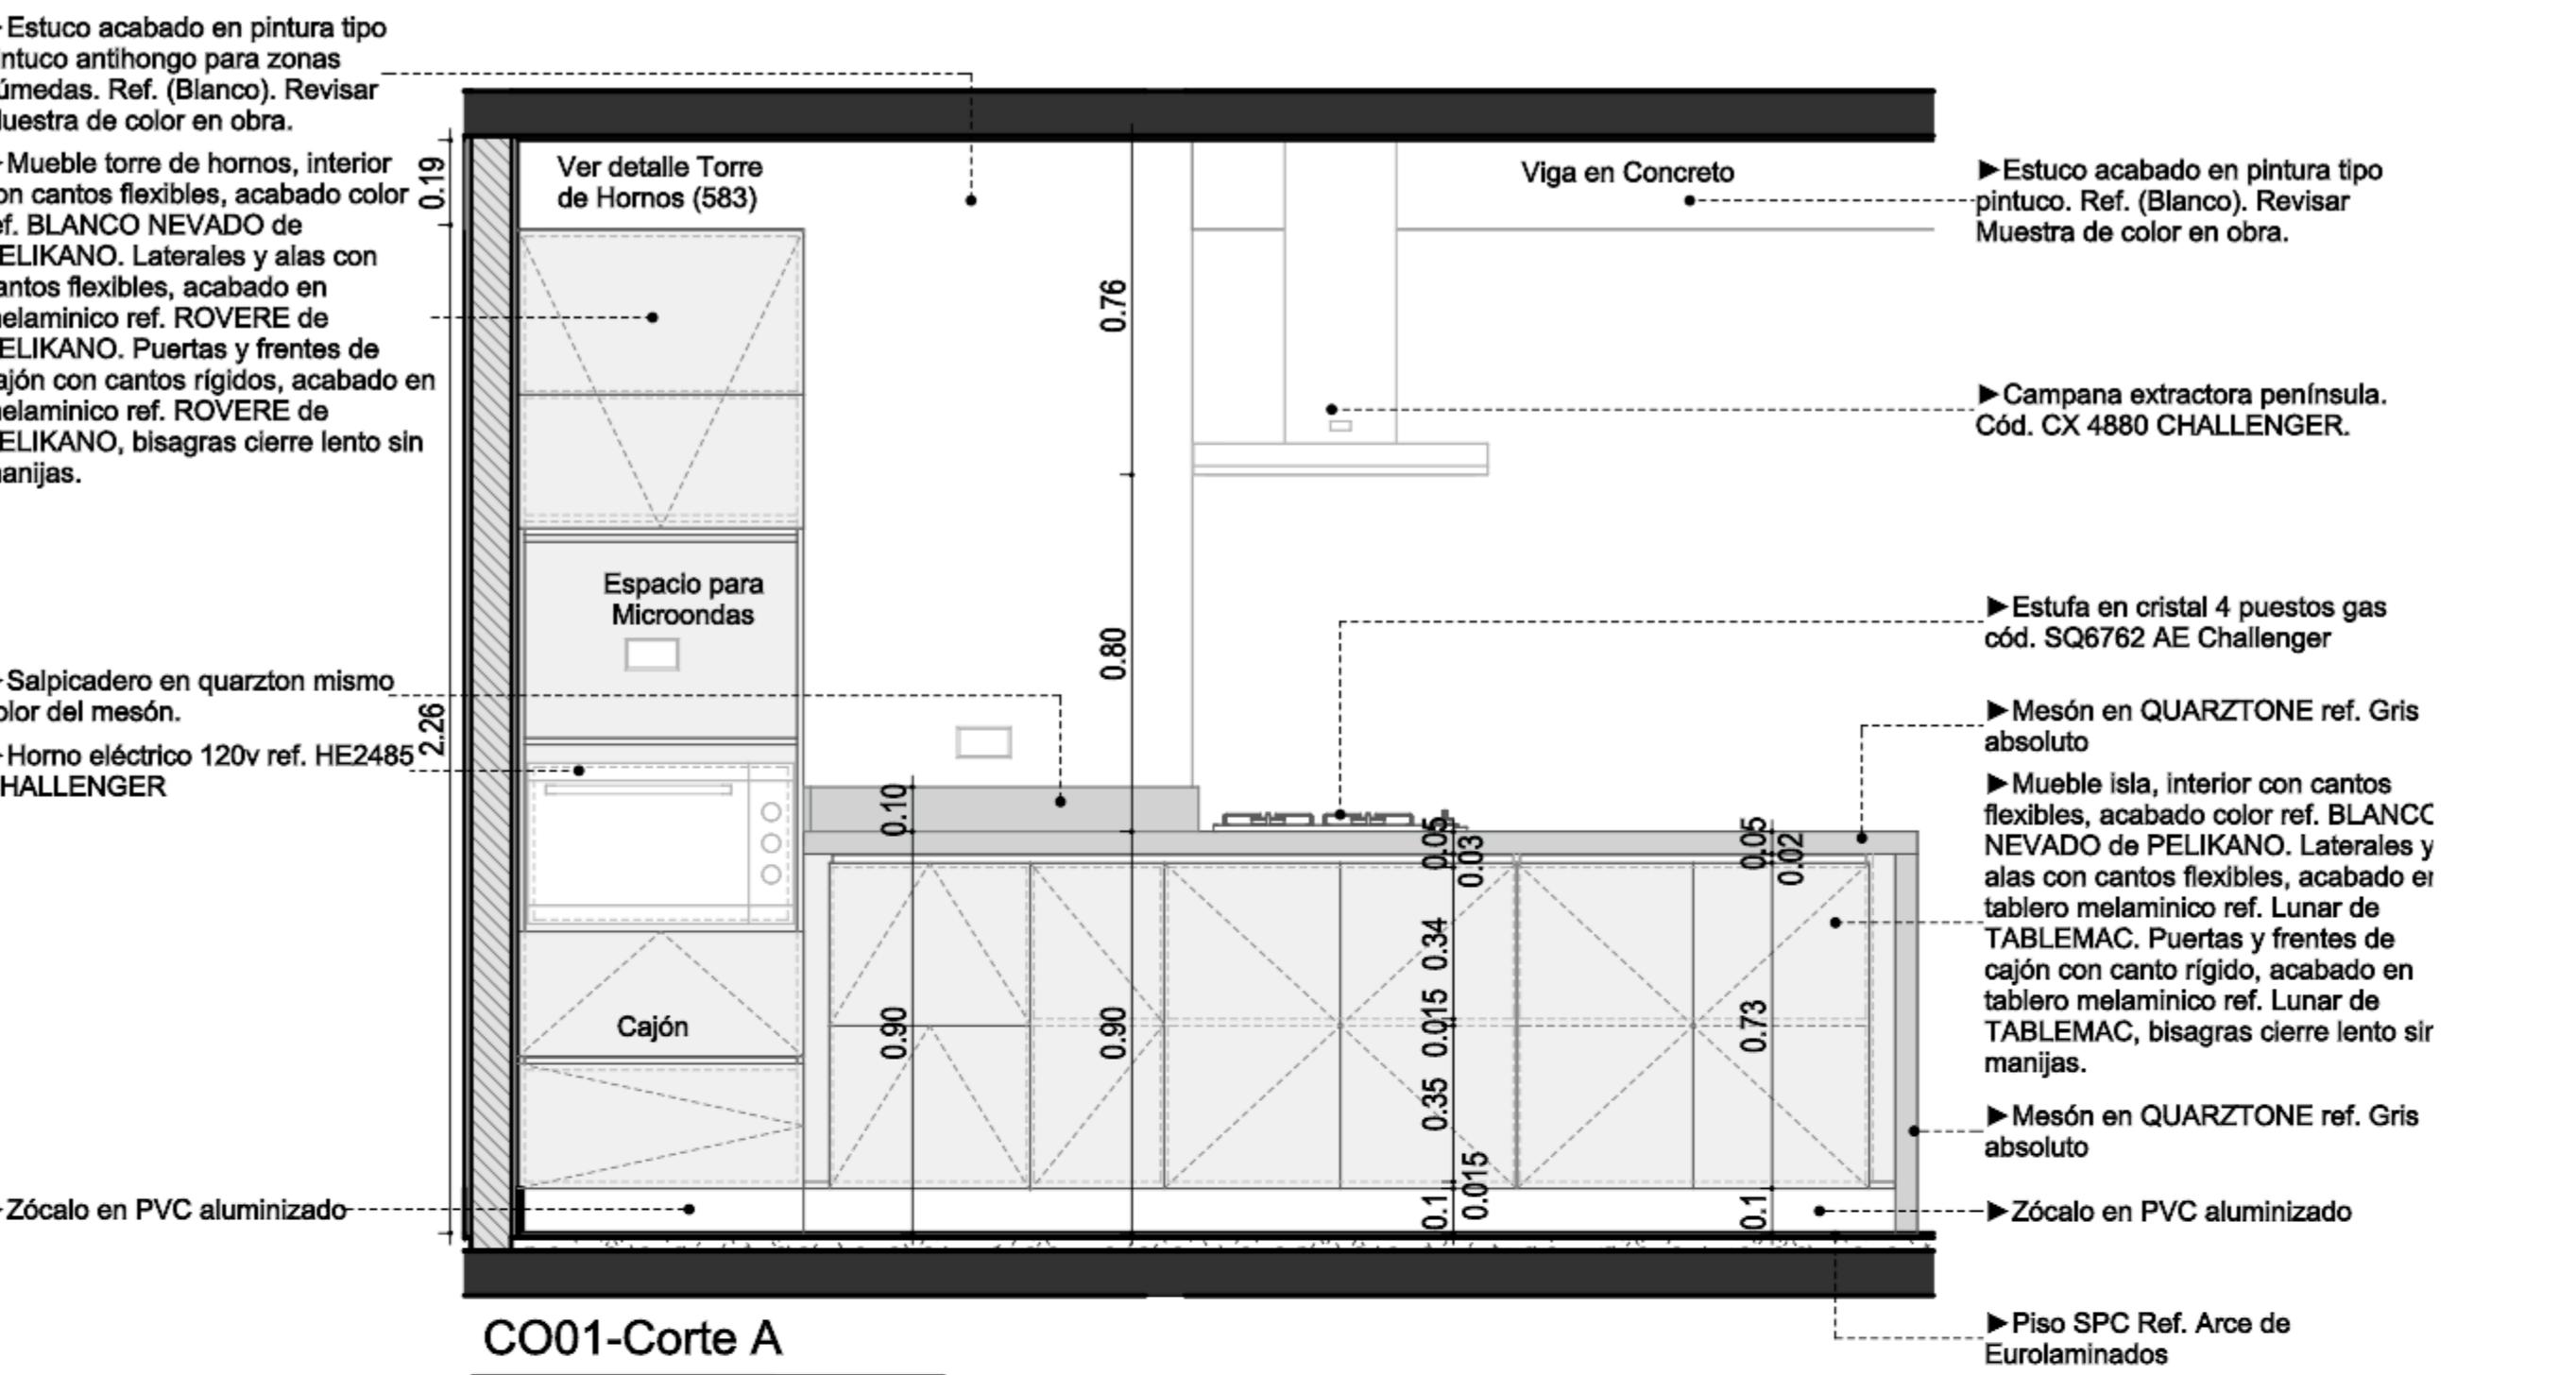

Detalle Estufa de Inducción
 1 : 25 Detalle de Cocinas

NOTA:
 01. Este detalle solo aplica para las cocinas en las que se deba instalar estufa de inducción por elección del cliente.

Nota: Pendiente definir por parte de AMARILLO, la apertura y herramientas de las puertas del mueble superior