
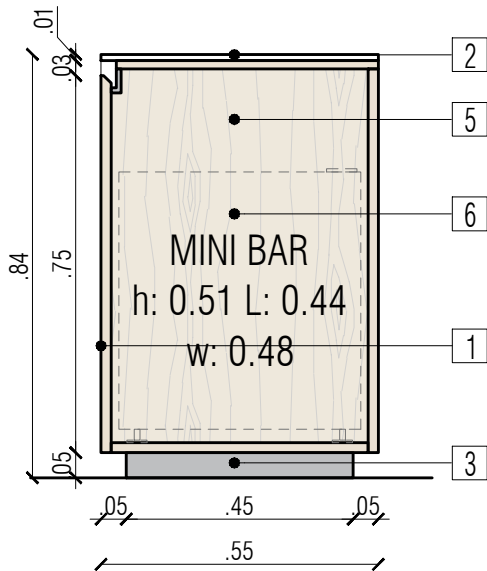
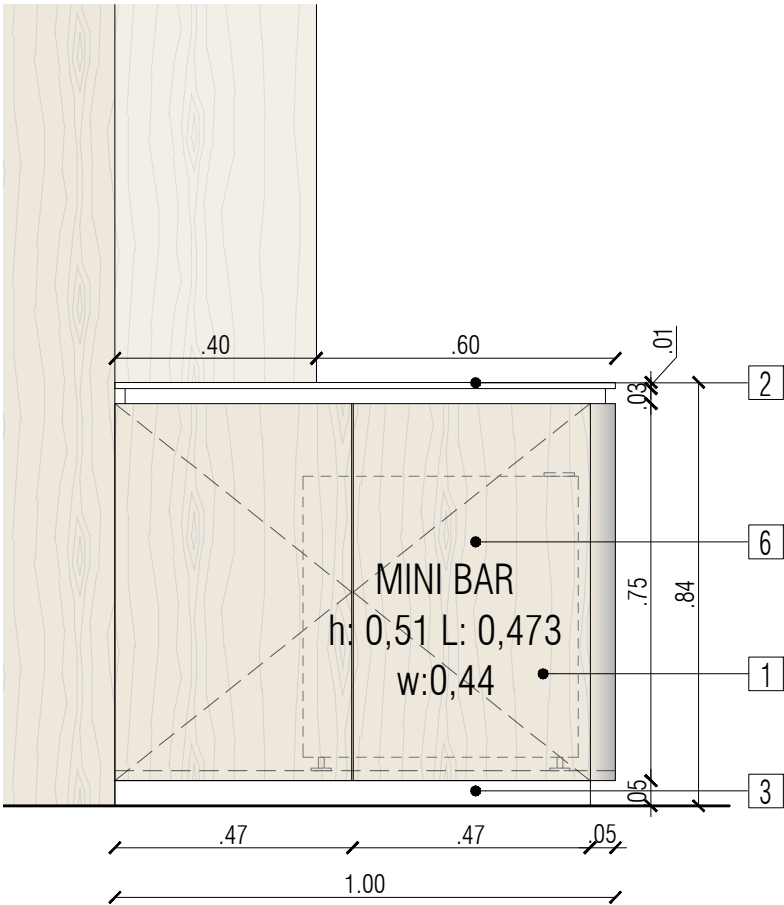


ESTANDARTIPOLOGÍA 4 - DETALLE MUEBLE MINIBAR - M1
HABITACIÓN 204-304-404-504-604-704-803-903

HOTEL 90/11
ESCALA 1:15

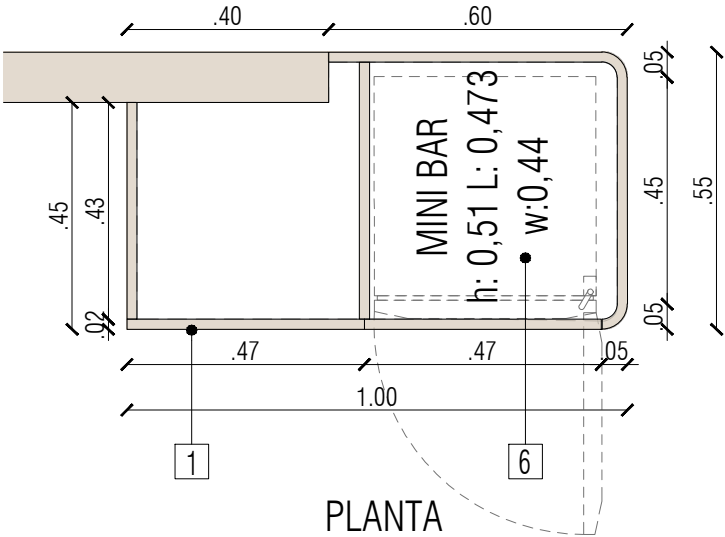

| ESPECIFICACIONES TIPOLOGÍA 4 - MUEBLES - M1-M2 | |
|--|---|
| 1 | Puertas de parche en melamina tipo madera clara Soder de duratex |
| 2 | Estructura mesón en melamina tipo madera soder + Tapa en formica CLAY PW |
| 3 | Zócalo acabado en |
| 4 | Entrepaños en melamina tipo lino remetido 5cm de la puerta |
| 5 | Interior en melamina tipo lino |
| 6 | Minibar: dim sugeridas: h: 0,59 L: 0,55 w:0,55. |
| 7 | Entrepañó reforzado para ubicación del minibar |
| 8 | Ventilación para minibar |
| 9 | Entrepañó superior en melamina tipo mader clara vienes de duratex o similar |
| 10 | Fondo falso |
| 11 | Dilatación contra piso/techo y costados de 2cm |
| 12 | Bolillo |
| 13 | Manija para closet de piso a techo según referencia |
| Nota: *Todas las dimensiones y especificaciones de materiales aqui plasmadas deberán ser verificadas por el contratista en sitio | |

entrecasa +
maria sanint

PBX: 3132960871-6018050138
CALLE 79A # 7A - 40
BOGOTÁ

PROYECTO

HOTEL 90/11

CONTIENE

ESTANDAR TIPOLOGÍA 4
DETALLE MUEBLE MINIBAR - M1

NOTAS

*LOS PLANOS
PRESENTADOS SON UN
DISEÑO ESTÉTICO MAS NO
TÉCNICO. EL CONTRATISTA
EN SITIO DEBE RECTIFICAR
TODAS LAS MEDIDAS Y DAR
GARANTÍA DE ESTABILIDAD
Y CALIDAD .
ESTOS DISEÑOS REQUIEREN
REVISIÓN POR PARTE DE
NOVENZA Y TÉCNICOS
INVOLUCRADOS. EL
PLANTEAMIENTO DE
ILUMINACIÓN, ELÉCTRICO Y
SANITARIO REQUIERE
APROBACIÓN Y REVISIÓN
POR PARTE DE TÉCNICO,
DISEÑADOR Y PROFESIONAL
EN EL CAMPO A CARGO

REVISIONES

| REVISIÓN | FECHA |
|----------|------------|
| - | 05/03/2025 |
| - | - |

DIBUJÓ:

DISEÑO:

Arq. Maria Sanint

CLIENTE:

REVISIÓN

PLANO:

P01

ESCALA:

INDICADAS