
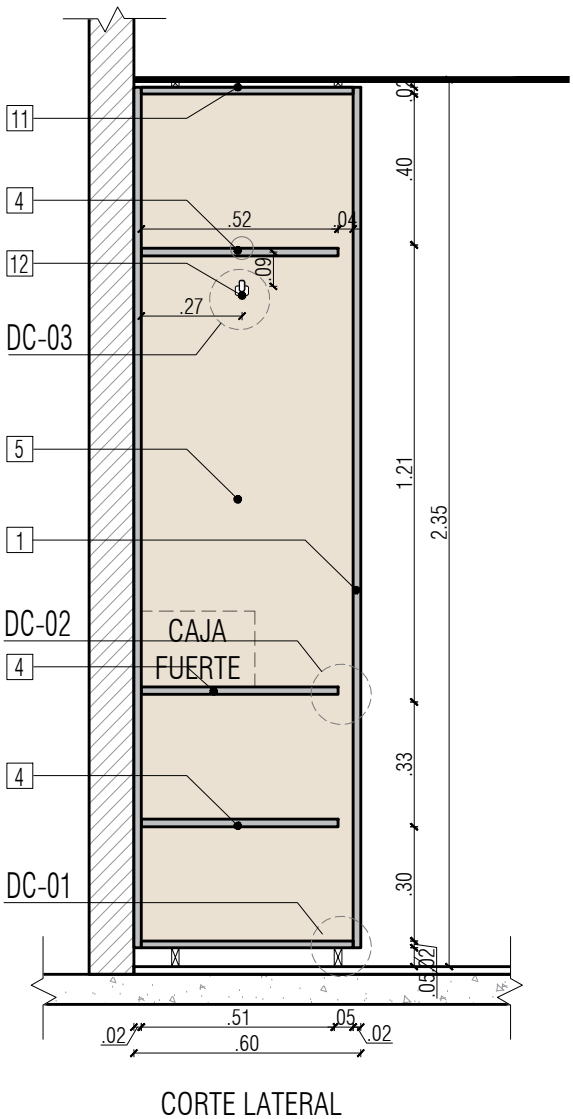
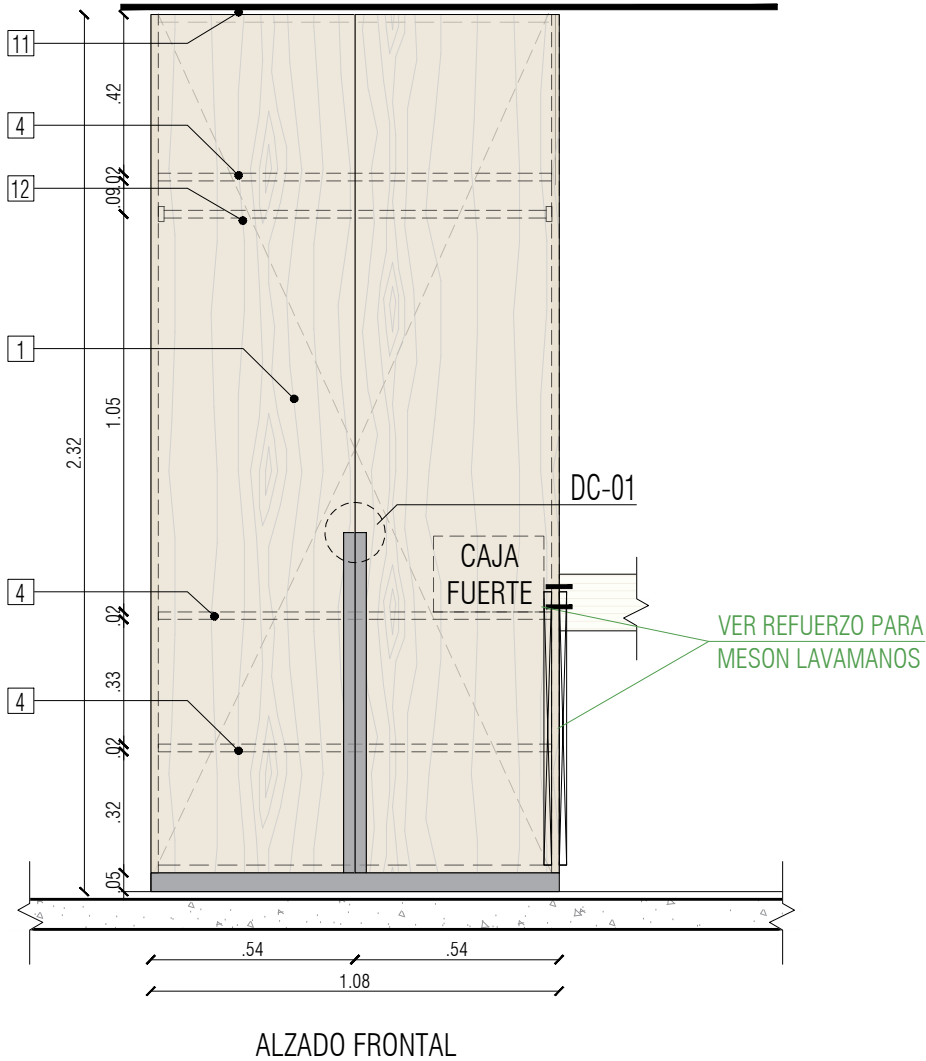


ESTANDARTIPOLOGÍA 4 - DETALLE MUEBLE CLOSET - M2  
HABITACIÓN 204-304-404-504-604-704-803-903

HOTEL 90/11  
ESCALA 1:20

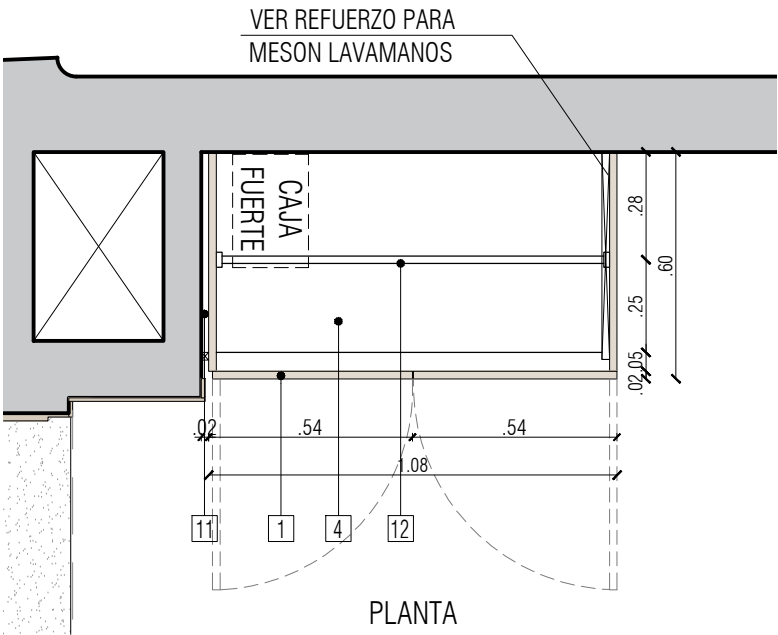

ESPECIFICACIONES TIPOLOGÍA 4 - MUEBLES - M1-M2	
1	Puertas de parche en melamina tipo madera clara Soder de duratex
2	Estructura mesón en melamina tipo madera soder + Tapa en formica CLAY PW
3	Zócalo acabado en
4	Entrepaños en melamina tipo lino remetido 5cm de la puerta
5	Interior en melamina tipo lino
6	Minibar: dim sugeridas: h: 0,59 L: 0,55 w:0,55.
7	Entrepaño reforzado para ubicación del minibar
8	Ventilación para minibar
9	Entrepaño superior en melamina tipo mader clara vienes de duratex o similar
10	Fondo falso
11	Dilatación contra piso/techo y costados de 2cm
12	Bolillo
13	Manija para closet de piso a techo según referencia
Nota: *Todas las dimensiones y especificaciones de materiales aqui plasmadas deberan ser verificadas por el contratisa en sitio	

entrecasa +  
maria sanint  
PBX: 3132960871-6018050138  
CALLE 79A # 7A - 40  
BOGOTÁ

PROYECTO

HOTEL 90/11

CONTIENE

ESTANDAR TIPOLOGÍA 4  
DETALLE MUEBLE CLOSET - M2

NOTAS

\*LOS PLANOS  
PRESENTADOS SON UN  
DISEÑO ESTÉTICO MAS NO  
TÉCNICO. EL CONTRATISTA  
EN SITIO DEBE RECTIFICAR  
TODAS LAS MEDIDAS Y DAR  
GARANTÍA DE ESTABILIDAD  
Y CALIDAD .  
ESTOS DISEÑOS REQUIEREN  
REVISIÓN POR PARTE DE  
NOVENZA Y TÉCNICOS  
INVOLUCRADOS. EL  
PLANTEAMIENTO DE  
ILUMINACIÓN, ELÉCTRICO Y  
SANITARIO REQUIERE  
APROBACIÓN Y REVISIÓN  
POR PARTE DE TÉCNICO,  
DISEÑADOR Y PROFESIONAL  
EN EL CAMPO A CARGO

REVISIONES

REVISIÓN	FECHA
-	05/03/2025
-	-

DIBUJÓ:

DISEÑO:

Arq. Maria Sanint

CLIENTE:

REVISIÓN

PLANO:

P01

ESCALA:

INDICADAS